
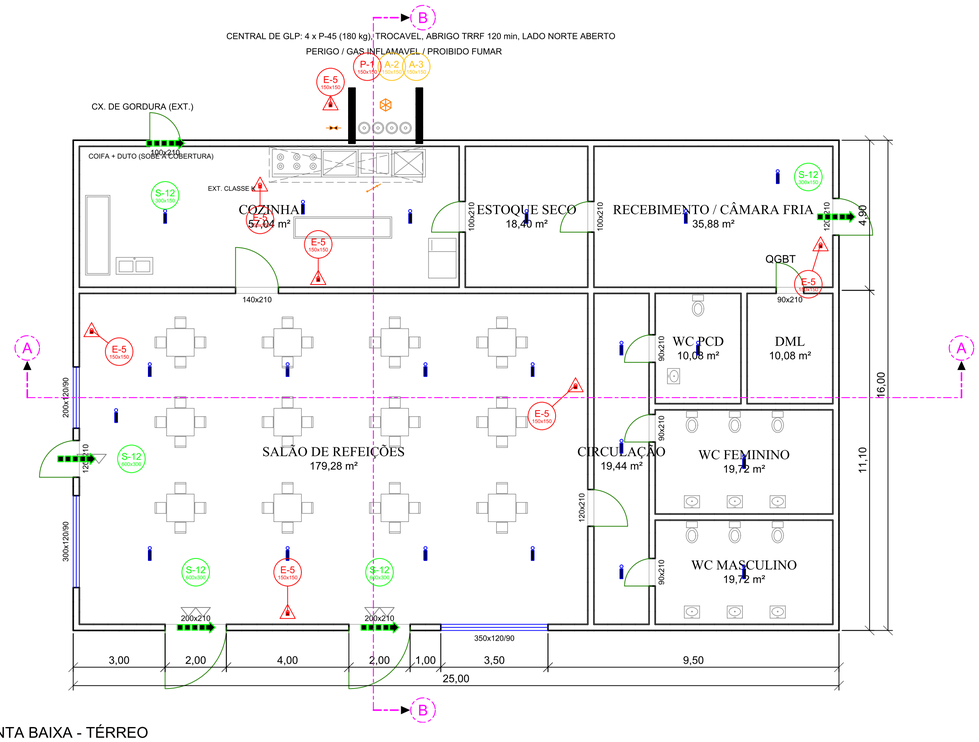



PLANTA BAIXA - TÉRREO
ESCALA 1:100

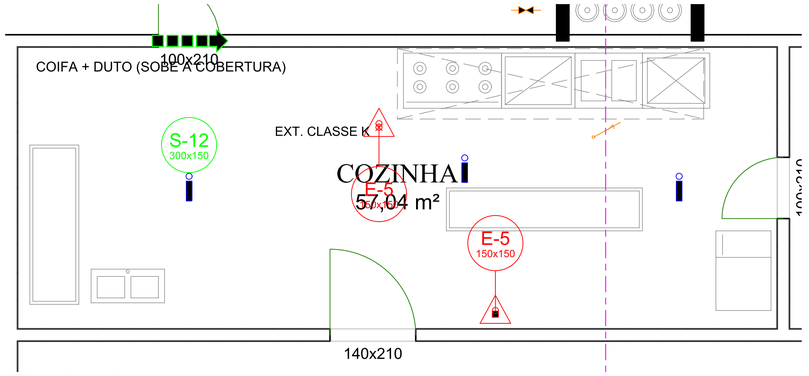

DETALHE - COZINHA
ESCALA 1:50

-45 (180 kg), TROCAVEL, ABRIG

IGO / GAS INFLAMAVEL / PROIB

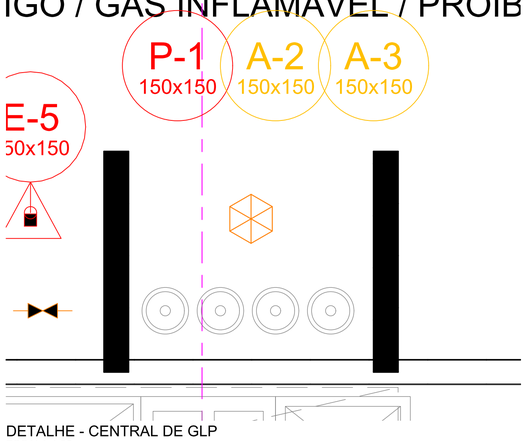

DETALHE - CENTRAL DE GLP
ESCALA 1:25

QUADRO DE ÁREAS

SALÃO DE REFEIÇÕES	179,28 m²
CIRCULAÇÃO	19,44 m²
WC MASCULINO	19,72 m²
WC FEMININO	19,72 m²
WC PCD	10,08 m²
DML	10,08 m²
COZINHA	57,04 m²
ESTOQUE SECO	18,40 m²
RECEBIMENTO / CÂMARA FRIA	35,88 m²
ÁREA ÚTIL TOTAL	369,64 m²
ÁREA CONSTRUÍDA (ATC)	400,00 m²

NOTAS

1. Cotas em metros; etiquetas de porta e janela em centímetros (largura x altura / peitoril).
2. Projeto fictício de exemplo: premissas de ocupação, alturas e tipo de construção não foram confirmadas.
3. Placas de sinalização (NT 2-05): dimensões das chamadas tiradas dos exemplos da Tabela 7; conferir pela distância de visualização.
4. Cozinha: duto de exaustão único e aparente, sem travessia de outros ambientes (NT 3-01, itens 2.1 e 2.2) - a confirmar com o projeto de exaustão.
5. Central de GLP: 4 recipientes P-45 em abrigo com paredes e cobertura TRRF 120 min, lado norte aberto (NT 3-02).

REV	DATA	DESCRIÇÃO
00	10/11/2026	Emissão inicial (exemplo)

OBRA	PROPRIETÁRIO / REPRESENTANTE LEGAL	AUTOR DO PROJETO E RESPONSÁVEL TÉCNICO	PRANCHA	ESCALA / DATA / REV
RESTAURANTE (F-8) - ATC 400,00 m² - EXEMPLO FICTÍCIO Endereço fictício	Proprietário fictício	Projeto fictício gerado pelo motor COSCIP	PLANTA BAIXA - TÉRREO E DETALHES	ESCALA 1:25 / 1:50 / 1:100 DATA 10/11/2026 REV 00 FOLHA 1/3

RASCUNHO GERADO PELO MOTOR COSCIP - SEM VALOR NORMATIVO - SEM RESPONSÁVEL TÉCNICO

QUADRO RESUMO

IDENTIFICAÇÃO DA EDIFICAÇÃO E/OU ÁREA DE RISCO		
Endereço: Endereço fictício		
Proprietário: Proprietário fictício		
Responsável técnico de segurança:		
Conselho técnico:	Nº da matrícula:	
Decreto estadual adotado: Decreto nº 42/2018	Nº de pavimentos: 1	Ocupação do subsolo: Não há
Edificação construída ou licenciada anterior à vigência do Decreto nº 42/2018: SIM ( ) NÃO ( )		Ano de construção:
Lotação prevista: 351 pessoas (NT 2-08, Anexo A)		
Condicionamento de ar:		

CLASSIFICAÇÃO - DECRETO ESTADUAL Nº 42/2018 - ANEXO II			
Grupo	Ocupação	Divisão	Descrição
F	Local de reunião de público	F-8	Local para refeição

CLASSIFICAÇÃO QUANTO À CARGA DE INCÊNDIO - NT 1-04	
Risco: MÉDIO 1 (NT 1-04)	Carga de incêndio (MJ/m²):

ELEMENTOS ESTRUTURAIS - NT 2-19	
Estrutura portante:	
Estrutura de sustentação da cobertura:	
Profundidade do subsolo (m):	TRRF:
Aplicação de revestimento: SIM ( ) NÃO ( )	Material de proteção:

MEDIDAS DE SEGURANÇA CONTRA INCÊNDIO - DECRETO Nº 42/2018
(X) Tabela 2 do Anexo III
(X) Extintores
(X) Saídas de emergência
(X) Iluminação de emergência
(X) Sinalização de segurança
(X) Controle de materiais de acabamento

RISCOS ESPECIAIS - DECRETO Nº 42/2018
(X) Gás liquefeito de petróleo (central externa, NT 3-02)
(X) Cozinha profissional (NT 3-01), a confirmar

GÁS GLP/GN - NT 3-02 (recipientes desenhados)			
Recipiente	Capacidade individual	Nº	Capacidade total
Recipiente P-45	45 kg	4	180 kg
Total		4	180 kg

QUADRO DE ÁREAS (m²)		
Descrição	Térreo	Total
ATC	400,00	400,00
Área útil dos ambientes (do desenho)	369,64	369,64

SISTEMA DE PROTEÇÃO POR EXTINTORES - NT 2-01 (contados no desenho)		
Tipo e capacidade	Térreo	Total
PQS ABC (capacidade não informada)	6	6
Água pressurizada (AP) (capacidade não informada)	1	1
TOTAL	7	7

SISTEMA DE SINALIZAÇÃO DE EMERGÊNCIA - NT 2-05 (contada no desenho)			
Placa	Dimensões (mm)	Térreo	Total
A-2 - Cuidado, risco de incêndio	150x150	1	1
A-3 - Cuidado, risco de explosão	150x150	1	1
E-5 - Extintor de incêndio	150x150	7	7
P-1 - Proibido fumar	150x150	1	1
S-12 - Saída de emergência	300x150	2	2
S-12 - Saída de emergência	600x300	3	3

SISTEMA DE ILUMINAÇÃO DE EMERGÊNCIA - NT 2-06 (contados no desenho)		
Tipo	Térreo	Total
Ponto de iluminação de emergência	21	21

CONTROLE DE MATERIAIS DE ACABAMENTO E REVESTIMENTO - NT 2-20					
Elemento	Acabamento	Classe	Revestimento	Classe	Retardante de chamas
(materiais não informados)					

SAÍDAS DE EMERGÊNCIA - NT 2-08	
Lotação: 351	Tipo de edificação:
Grupo e divisão: F-8	Pavimento: Térreo
Saída única ( ) Mais de uma saída (X)	Tipo de escada: Sem escada
Capacidade da unidade de passagem: 100	Unidades de passagem projetadas: 8 (portas do salão: 3 + 3 + 2)
Saídas desenhadas: 5	Placas de saída desenhadas: 5

Rascunho gerado pelo motor COSCIP: dados informados pelo usuário e contagens do desenho; sem valor normativo.

QUADRO RESUMO
ESCALA 1:100

NOTAS

1. Dados de identificação, classificação, medidas e saídas informados no projeto de exemplo; quantidades de extintores, placas, iluminação, GLP e áreas contadas do desenho.
2. A conferência entre o desenho e os valores declarados está no retorno do motor (quadro_resumo.conferencia).

OBRA
RESTAURANTE (F-8) - ATC 400,00 m² - EXEMPLO FICTÍCIO
Endereço fictício

PROPRIETÁRIO / REPRESENTANTE LEGAL
Proprietário fictício

AUTOR DO PROJETO E RESPONSÁVEL TÉCNICO
Projeto fictício gerado pelo motor COSCIP


PRANCHA
QUADRO RESUMO

ESCALA / DATA / REV
ESCALA 1:100
DATA 10/11/2026
REV 00
FOLHA 2/3

RASCUNHO GERADO PELO MOTOR COSCIP - SEM VALOR NORMATIVO - SEM RESPONSÁVEL TÉCNICO


FACHADA NORTE

ESCALA 1:100

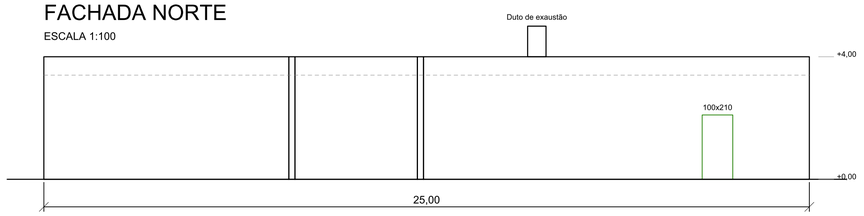


FACHADA SUL

ESCALA 1:100

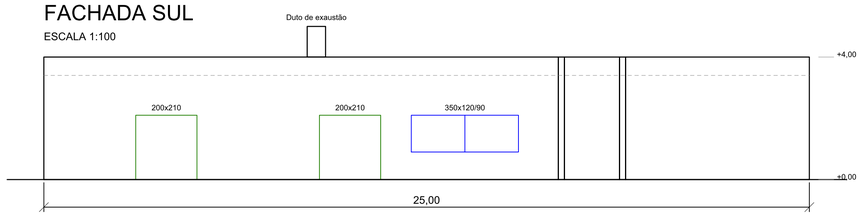


CORTE B-B

ESCALA 1:100

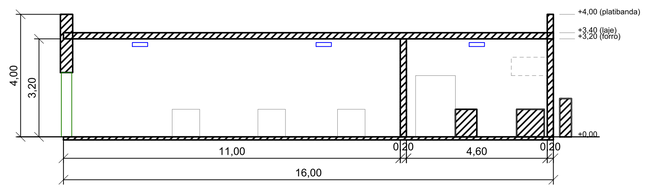

CORTE A-A

ESCALA 1:100

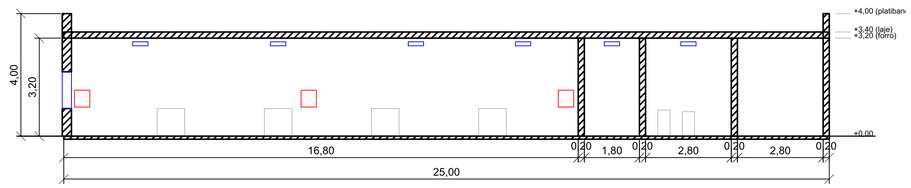

CORTES E FACHADAS

ESCALA 1:100

NOTAS

1. Cortes e fachadas gerados da mesma geometria da planta; alturas e peitoris são premissas do exemplo (projeto fictício).
2. Sem remoção de linhas ocultas.

OBRA	PROPRIETÁRIO / REPRESENTANTE LEGAL	AUTOR DO PROJETO E RESPONSÁVEL TÉCNICO	PRANCHA	ESCALA / DATA / REV
RESTAURANTE (F-8) - ATC 400,00 m² - EXEMPLO FICTÍCIO Endereço fictício	Proprietário fictício	Projeto fictício gerado pelo motor COSCIP	CORTES E FACHADAS	ESCALA 1:100 DATA 10/11/2026 REV 00 FOLHA 3/3

RASCUNHO GERADO PELO MOTOR COSCIP - SEM VALOR NORMATIVO - SEM RESPONSÁVEL TÉCNICO