
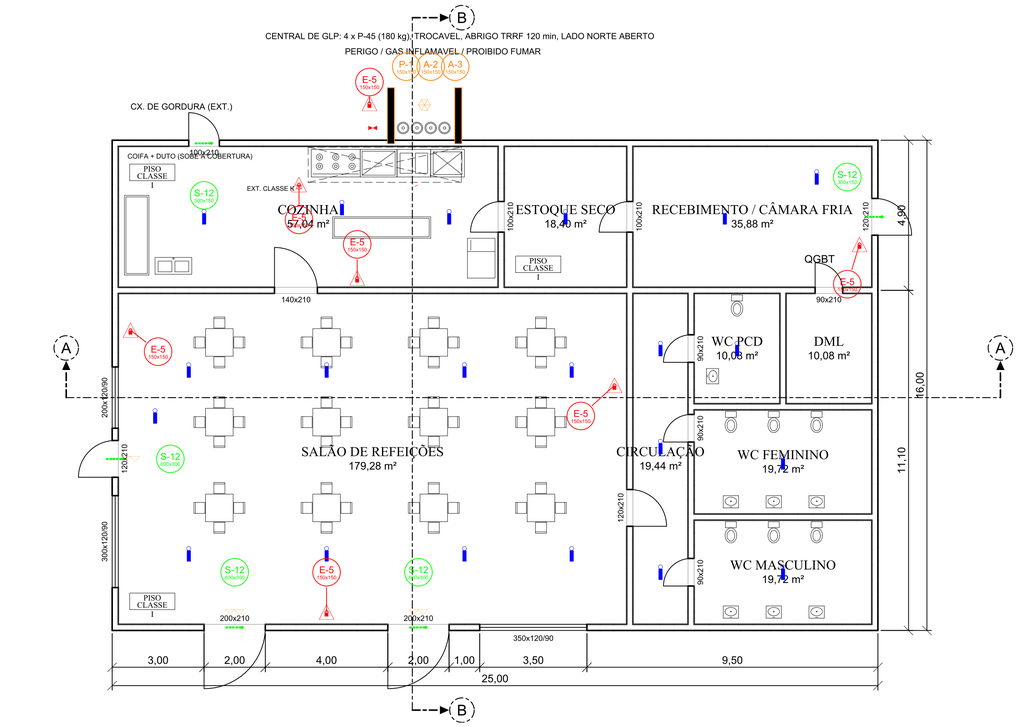



1 PLANTA BAIXA - TÉRREO
ESCALA 1:100

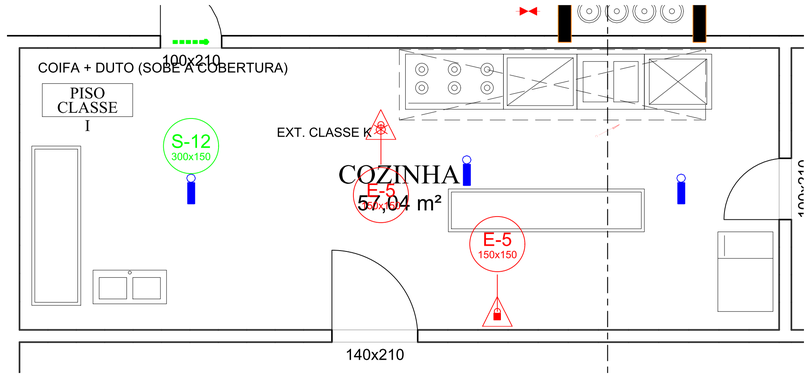

2 DETALHE - COZINHA
ESCALA 1:50

-45 (180 kg), TROCAVEL, ABRIG

IGO / GAS INFLAMAVEL / PROIB

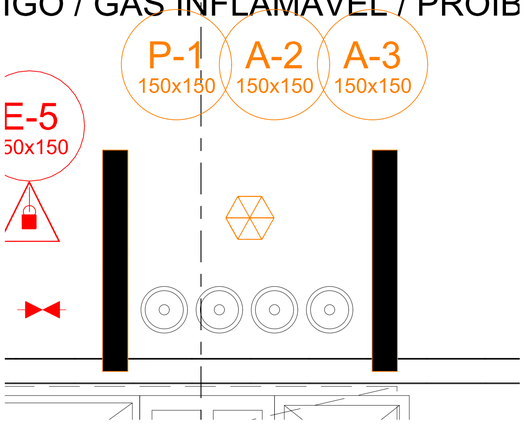

3 DETALHE - CENTRAL DE GLP
ESCALA 1:25

QUADRO DE ÁREAS

SALÃO DE REFEIÇÕES	179,28 m²
CIRCULAÇÃO	19,44 m²
WC MASCULINO	19,72 m²
WC FEMININO	19,72 m²
WC PCD	10,08 m²
DML	10,08 m²
COZINHA	57,04 m²
ESTOQUE SECO	18,40 m²
RECEBIMENTO / CÂMARA FRIA	35,88 m²
ÁREA ÚTIL TOTAL	369,64 m²
ÁREA CONSTRUÍDA (ATC)	400,00 m²

NOTAS

1. Cotas em metros; etiquetas de porta e janela em centímetros (largura x altura / peitoril).
2. Projeto fictício de exemplo: premissas de ocupação, alturas e tipo de construção não foram confirmadas.
3. Placas de sinalização (NT 2-05): dimensões das chamadas tiradas dos exemplos da Tabela 7; conferir pela distância de visualização.
4. Cozinha: duto de exaustão único e aparente, sem travessia de outros ambientes (NT 3-01, itens 2.1 e 2.2) - a confirmar com o projeto de exaustão.
5. Central de GLP: 4 recipientes P-45 em abrigo com paredes e cobertura TRRF 120 min, lado norte aberto (NT 3-02).

REV	DATA	DESCRIÇÃO
00	10/11/2026	Emissão inicial (exemplo)

PROJETO DE SEGURANÇA CONTRA INCÊNDIO E PÂNICO
RESTAURANTE (F-8) - ATC 400,00 M² - EXEMPLO FICTÍCIO

CONTEÚDO: PLANTA BAIXA - TÉRREO E DETALHES

Nº DA PRANCHA: 01 DE 06

PROPRIETÁRIO: PROPRIETÁRIO FICTÍCIO

ENDEREÇO: ENDEREÇO FICTÍCIO

ESCALA:	DATA:	ÁREA:	REVISÃO:
INDICADA	10/11/2026	400,00 m²	00

PROPRIETÁRIO
PROPRIETÁRIO FICTÍCIO

O AUTOR DO LEV. ARQUITETÔNICO

O AUTOR DO PROJETO DE SEGURANÇA
PROJETO FICTÍCIO GERADO PELO MOTOR COSCIP

APROVAÇÃO CORPO DE BOMBEIROS:

RASCUNHO GERADO PELO MOTOR COSCIP - SEM VALOR NORMATIVO - SEM RESPONSÁVEL TÉCNICO

QUADRO RESUMO

IDENTIFICAÇÃO DA EDIFICAÇÃO E/OU ÁREA DE RISC			
Endereço: Endereço fictício			
Proprietário: Proprietário fictício			
Responsável técnico de segurança:			
Conselho Técnico:			nº de matrícula:
Decreto Estadual adotado (nº e ano): Decreto nº 42/2018	Altura (m):	Nº de pavimentos: 1	Ocupação do subsolo: Não hu
Edificação construída ou licenciada anterior à vigência do Decreto nº 42/2018:		SIM ( ) NÃO ( )	Ano da construção ou do licer
Lotação prevista (apenas para áreas que desenvolvam ocupação do Grupo F): 351 pessoas (NT 2-(			
Descreva como se dá o sistema de condicionamento de ar da edificação (central de ar, split, etc.):			

CLASSIFICAÇÃO – Decreto Estadual nº 42/2018 - Anexo			
Grupo	Ocupação	Divisão	
F	Local de reunião de público	F-8	Lo

CLASSIFICAÇÃO DAS EDIFICAÇÕES E ÁREAS DE RISCO QUANTO A CARGA	
Risco	Carga de incêndio (MJ/m²) (Ap
MÉDIO 1 (NT 1-04)	

ELEMENTOS ESTRUTURAIS – NT 2-19			
Estrutura portante (ex: concreto, aço, madeira, outros):			
Estrutura de sustentação da cobertura (ex: concreto, aço, madeira, outros):			
Profundidade do subsolo (m):		TRRF:	
Aplicação de revestimento	SIM ( ) NÃO ( )	Tipo de material de proteção: (Conforme modelo do	

MEDIDAS DE SEGURANÇA CONTRA INCÊNDIO – DECRETO N	
	Tabela adotada, conforme anexo III do Decreto nº 42/2018
X	Tabela 2 do Anexo III
X	Extintores
X	Saídas de emergência
X	Iluminação de emergência
X	Sinalização de segurança
X	Controle de materiais de acabamento

RISCOS ESPECIAIS – DECRETO Nº 42/2018	
X	Gás liquefeito de petróleo (central externa, NT 3-02)
X	Cozinha profissional (NT 3-01), a confirmar

RESERVATÓRIO/RTI			
Localização	Tipo de Sucção	Vol. do Reservatório	Vc

BOMBA DE INCÊNDIO – NT 2-04			
	Tipo	Vazão (L/MIN)	F

SISTEMA DE HIDRANTES E MANGOTINHOS – NT 2-02	
Classificação de Risco	
Diâmetro da Tubulação de Sucção (mm)	
Diâmetro da Tubulação Recalque (mm)	
Diâmetro da Mangueira (mm)	
Tipo da Mangueira	
Tipo de Esguicho	
Hidrante de Recalque	

GÁS GLP/GN – NT 3-02			
Abastecimento por gás combustível:			
Tipo de Cilindro/Botijão	Capacidade Individual	Nº de Cilindros	
Estacionário (Kg)			
Transportável P-45 (Kg)	45	4	

QUADRO DE ÁREAS		
Descrição	Térreo	
ATC (m²)	400,00	

SISTEMA DE PROTEÇÃO POR EXTINTORES – NT 2-0		
Tipo e capacidade	Térreo	
PQS ABC (capacidade não informada)	6	
Água pressurizada (AP) (capacidade não informada)	1	
Total	7	

POSICIONAMENTO DOS HIDRANTES – NT 2-02		
	Térreo	
(nenhum hidrante desenhado)		

SISTEMA DE SINALIZAÇÃO DE EMERGÊNCIA – NT 2-0			
Código da Placa	Dimensões (mm)	Térreo	
Placa P-1	150x150	1	
Placa A-2	150x150	1	
Placa A-3	150x150	1	
Placa S-12	300x150	2	
Placa S-12	600x300	3	
Placa E-5	150x150	7	

SISTEMA DE ILUMINAÇÃO DE EMERGÊNCIA – NT 2-0		
Tipo	Térreo	
Ponto de iluminação de emergência	21	

1 QUADRO RESUMO
ESCALA 1:100

NOTAS

1. Dados de identificação, classificação, medidas e saídas informados no projeto de exemplo; quantidades de extintores, placas, iluminação, GLP e áreas contadas do desenho.
2. A conferência entre o desenho e os valores declarados está no retorno do motor (quadro_resumo.conferencia).

PROJETO DE SEGURANÇA CONTRA INCÊNDIO E PÂNICO
RESTAURANTE (F-8) - ATC 400,00 M² - EXEMPLO FICTÍCIO

CONTEÚDO: QUADRO RESUMO

Nº DA PRANCHA: 02 DE 06

PROPRIETÁRIO: PROPRIETÁRIO FICTÍCIO

ENDEREÇO: ENDEREÇO FICTÍCIO

ESCALA:	DATA:	ÁREA:	REVISÃO:
1:100	10/11/2026		00

PROPRIETÁRIO
PROPRIETÁRIO FICTÍCIO

O AUTOR DO LEV. ARQUITETÔNICO


O AUTOR DO PROJETO DE SEGURANÇA
PROJETO FICTÍCIO GERADO PELO MOTOR COSCIP

APROVAÇÃO CORPO DE BOMBEIROS:

RASCUNHO GERADO PELO MOTOR COSCIP - SEM VALOR NORMATIVO - SEM RESPONSÁVEL TÉCNICO


FACHADA NORTE

ESCALA 1:100

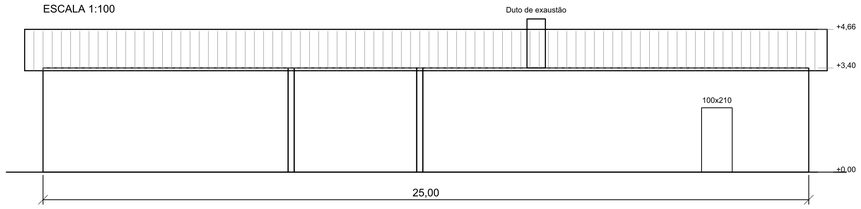


FACHADA SUL

ESCALA 1:100

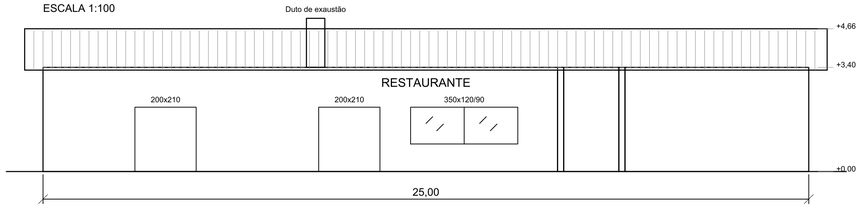


CORTE B-B

ESCALA 1:100

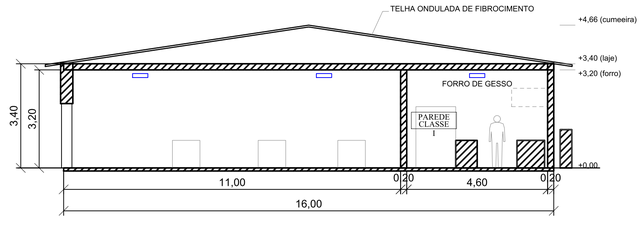

CORTE A-A

ESCALA 1:100

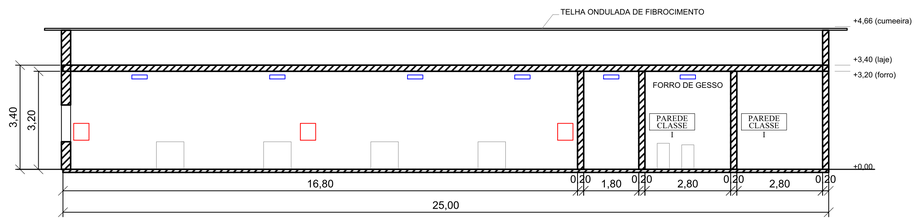

1 CORTES E FACHADAS
ESCALA 1:100

NOTAS

1. Cortes e fachadas gerados da mesma geometria da planta; alturas, telhado e classes dos materiais são premissas do exemplo (projeto fictício).

CÁLCULO DA LARGURA DAS SAÍDAS (NT 2-08)

- Ocupação F-8 (local para refeição): 1 pessoa por m² de área (Anexo A).
- Área atendida pela descarga: 350,48 m² -> P = 351 pessoas.
- C = 100 pessoas por unidade de passagem (acessos e descarga).
- N = 351 / 100 = 3,51 -> 4 unidades de passagem.
- Largura mínima = 4 x 0,55 = 2,20 m.
- Largura projetada: portas de 1,20 + 1,20 m = 2,40 m (>= 2,20 m).

PROJETO DE SEGURANÇA CONTRA INCÊNDIO E PÂNICO
RESTAURANTE (F-8) - ATC 400,00 M² - EXEMPLO FICTÍCIO

CONTEÚDO:
CORTES E FACHADAS

Nº DA PRANCHA:
03
DE 06

PROPRIETÁRIO:
PROPRIETÁRIO FICTÍCIO

ENDEREÇO:
ENDEREÇO FICTÍCIO

ESCALA:	DATA:	ÁREA:	REVISÃO:
1:100	10/11/2026		00


PROPRIETÁRIO
PROPRIETÁRIO FICTÍCIO

O AUTOR DO LEV. ARQUITETÔNICO

O AUTOR DO PROJETO DE SEGURANÇA
PROJETO FICTÍCIO GERADO PELO MOTOR COSCIP

APROVAÇÃO CORPO DE BOMBEIROS:

RASCUNHO GERADO PELO MOTOR COSCIP - SEM VALOR NORMATIVO - SEM RESPONSÁVEL TÉCNICO

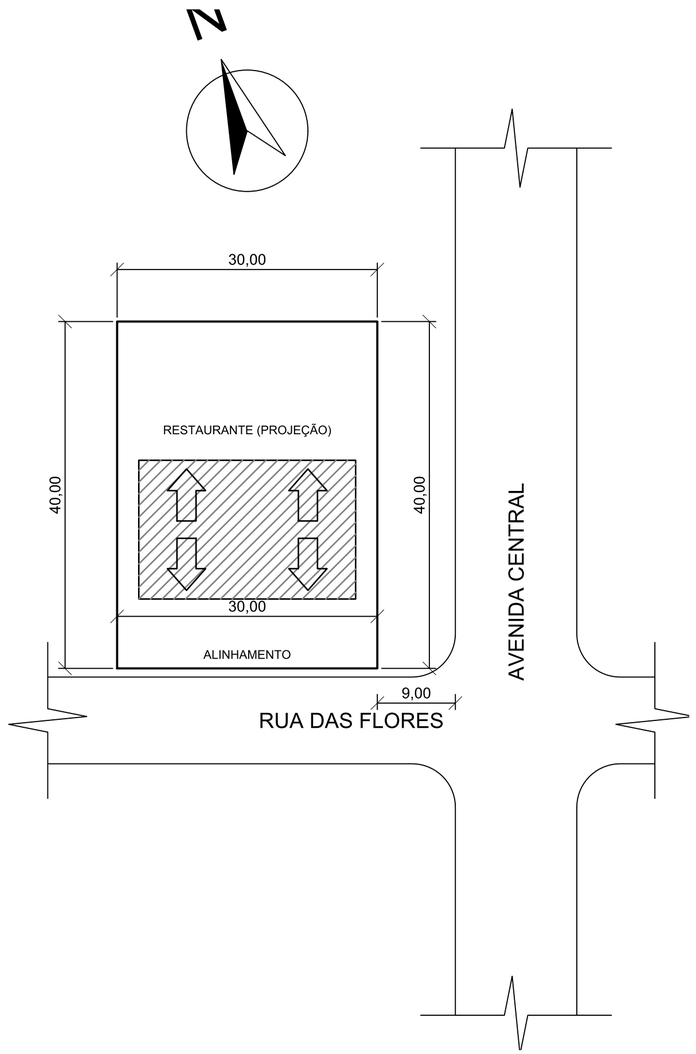

1 PLANTA DE SITUAÇÃO
ESCALA 1:500

NOTAS

1. Lote, ruas, distância à esquina e norte são premissas do exemplo (projeto fictício).

PROJETO DE SEGURANÇA CONTRA INCÊNDIO E PÂNICO
RESTAURANTE (F-8) - ATC 400,00 M² - EXEMPLO FICTÍCIO

CONTEÚDO:
PLANTA DE SITUAÇÃO

Nº DA PRANCHA:
04
DE 06

PROPRIETÁRIO:
PROPRIETÁRIO FICTÍCIO

ENDEREÇO:
ENDEREÇO FICTÍCIO

ESCALA:	DATA:	ÁREA:	REVISÃO:
1:500	10/11/2026		00

PROPRIETÁRIO
PROPRIETÁRIO FICTÍCIO

O AUTOR DO LEV. ARQUITETÔNICO


O AUTOR DO PROJETO DE SEGURANÇA
PROJETO FICTÍCIO GERADO PELO MOTOR COSCIP

APROVAÇÃO CORPO DE BOMBEIROS:

RASCUNHO GERADO PELO MOTOR COSCIP - SEM VALOR NORMATIVO - SEM RESPONSÁVEL TÉCNICO

DETALHE - INSTALAÇÃO DO EXTINTOR

ESCALA 1:15

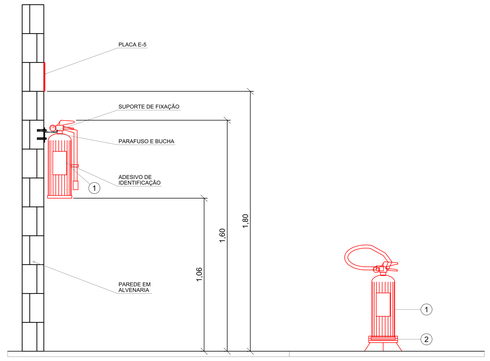

NA PAREDE NO PISO

PLACA E-5 (AMPLIADA, SEM ESCALA)



SÍMBOLO: QUADRADA
CÓDIGO: E-5
FUNDO: VERMELHA
PICTOGRAMA: FOTOLUMINESCENTE
DIMENSÃO: 200 x 200 mm
NT 2-05, TABELA 6

Nº	DESCRIÇÃO
1	EXTINTOR PQS ABC 6 KG
2	SUPORTE PARA EXTINTOR NO PISO


NOTAS:
1. ALÇA DE MANUSEIO A NO MÁXIMO 1,60 m DO PISO ACABADO (NT 2-01, 5.2.1 b).
2. PARTE INFERIOR A NO MÍNIMO 0,10 m DO PISO; O EXTINTOR NÃO FICA EM CONTATO COM O PISO: NO PISO, SOBRE SUPORTE (NT 2-01, 5.2.1 b e c).
3. SUPORTE RESISTENTE A 3 VEZES A MASSA TOTAL DO EXTINTOR (NT 2-01, 5.2.1 a).
4. PLACA E-5 NO NÍVEL SUPERIOR: BASE A NO MÍNIMO 1,60 m DO PISO (NT 2-05, 4.7; NT 2-05, Tabela 6).
5. EXTINTOR REPRESENTADO COM Ø 0,16 x 0,54 m (TAMANHO APROXIMADO: CONFIRMAR COM O FABRICANTE).

1 DETALHE 1 - EXTINTOR

ESCALA 1:15

DETALHE - BLOCO AUTÔNOMO DE ILUMINAÇÃO

ESCALA 1:20

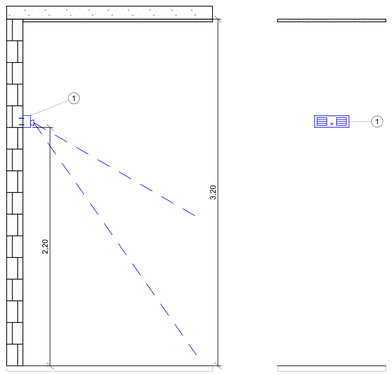

Nº	DESCRIÇÃO
1	BLOCO AUTÔNOMO DE ILUMINAÇÃO DE EMERGÊNCIA: 300 lm, AUTONOMIA MÍNIMA 60 min

NOTAS:
1. AUTONOMIA MÍNIMA DE 60 min (NT 2-06, 5.2); DIVISÃO F-8.
2. INSTALAÇÃO, NÍVEL DE ILUMINAMENTO E DISTÂNCIA ENTRE PONTOS PELA NBR 10898:2013, ADOTADA PELA NT (NT 2-06, 5.1.1).
3. NAS ESCADAS: UM PONTO NO NÍVEL DO PAVIMENTO E OUTRO NO PATAMAR INTERMEDIÁRIO, SEM PONTO DE SOMBRA (NT 2-06, 5.3.2).
4. ALTURA DE INSTALAÇÃO 2,20 m (INFORMADA); FACHO DE LUZ ILUSTRATIVO.

2 DETALHE 2 - BLOCO AUTÔNOMO

ESCALA 1:20

DETALHE - INSTALAÇÃO DA SINALIZAÇÃO

ESCALA 1:25

PLACA S-12 (AMPLIADA, SEM ESCALA)

SÍMBOLO: RETANGULAR
CÓDIGO: S-12
FUNDO: VERDE
PICTOGRAMA: FOTOLUMINESCENTE
LETRA: ACIMA DE 50 mm
DIMENSÃO: 252 x 136 mm
NT 2-05, TABELA 5

NOTAS:
1. NÍVEL SUPERIOR: BASE DA PLACA A NO MÍNIMO 1,80 m DO PISO ACABADO OU NO TETO (NT 2-05, 4.7).
2. PLACA S-12 SOBRE A PORTA DE SAÍDA, NO NÍVEL SUPERIOR (NT 2-05, Tabela 5).
3. NÍVEL INFERIOR: NO PISO OU A NO MÁXIMO 0,50 m (NT 2-05, 4.5).
4. PORTA REPRESENTADA COM 0,90 x 2,10 m E PÉ-DIREITO 3,00 m: VALEM AS MEDIDAS DA PLANTA.

3 DETALHE 3 - SINALIZAÇÃO

ESCALA 1:25

NOTAS
1. Detalhes cotados com as medidas das NTs citadas em cada nota; alturas do bloco autônomo e pé-direito são premissas do exemplo (projeto fictício).

PROJETO DE SEGURANÇA CONTRA INCÊNDIO E PÂNICO
RESTAURANTE (F-8) - ATC 400,00 M² - EXEMPLO FICTÍCIO

CONTEÚDO: DETALHES DE INSTALAÇÃO

Nº DA PRANCHA: 05 DE 06

PROPRIETÁRIO: PROPRIETÁRIO FICTÍCIO

ENDEREÇO: ENDEREÇO FICTÍCIO

ESCALA:	DATA:	ÁREA:	REVISÃO:
INDICADA	10/11/2026		00

PROPRIETÁRIO
PROPRIETÁRIO FICTÍCIO

O AUTOR DO LEV. ARQUITETÔNICO


O AUTOR DO PROJETO DE SEGURANÇA
PROJETO FICTÍCIO GERADO PELO MOTOR COSCIP

APROVAÇÃO CORPO DE BOMBEIROS:


RASCUNHO GERADO PELO MOTOR COSCIP - SEM VALOR NORMATIVO - SEM RESPONSÁVEL TÉCNICO

DETALHE - CENTRAL DE GLP

ESCALA 1:25

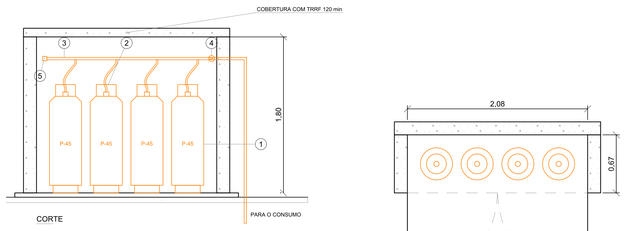

CORTE

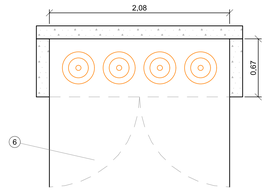

PLANTA

NOTAS:

1. CENTRAL NO TÉRREO, FORA DA PROJEÇÃO DA EDIFICAÇÃO. EM LOCAL VENTILADO (NT 3-02, 5.2.1); RECIPIENTES A NO MÍNIMO 1,00 m DE RALOS, CANALETAS E CAIXAS (NT 3-02, 5.2.5).
2. CAPACIDADE 180 kg (= 90 kg): PAREDES E COBERTURA COM TRRF DE NO MÍNIMO 120 min; PISO EM CONCRETO COM NO MÍNIMO 0,05 m; ALTURA INTERNA ÚTIL MÍNIMA 1,80 m (NT 3-02, 5.3.2).
3. LADO MAIOR ABERTO COM PORTAS INCOMBUSTÍVEIS ABRINDO PARA FORA; VENTILAÇÃO PERMANENTE DE NO MÍNIMO 0,64 m² (MAIOR ENTRE 10% DA PLANTA E 0,32 × 0,32 m²) (NT 3-02, 5.3.2).
4. RECIPIENTES LADO A LADO, EM ATÉ DUAS LINHAS (NT 3-02, 5.3.5).
5. PLACA DE PERIGO (0,95 m × 0,48 m) A NO MÁXIMO 10 m DE RECIPIENTES, PERIGO / GÁS INFLAMÁVEL / PROIBIDO FUMAR, FOTOLUMINESCENTE, VISÍVEL DE QUALQUER ACESSO (NT 3-02, 5.4.5).
6. SINALIZAÇÃO 1 EXTINTOR (BC) OU PQS DE NO MÍNIMO 10 m DA CENTRAL (NT 3-02, Tabela 3, NT 3-02, 5.4.2).
7. TUBULAÇÃO APARENTE DE GLP: FASE VAPOR AMARELA, FASE LÍQUIDA LARANJA (NT 3-02, Tabela 1).
8. RECIPIENTES REPRESENTADOS COM Ø 0,37 x 1,25 m (TAMANHO APROXIMADO); VÁLVULA DE RETENÇÃO E PIGTAILS CONFORME O PROJETO DA CENTRAL.

1 DETALHE 4 - CENTRAL DE GLP

ESCALA 1:25

PLACA DA CENTRAL (AMPLIADA 5x)




MEDIDAS MÍNIMAS 190 x 95 mm; COTAS NA AMPLIAÇÃO

Nº	DESCRIÇÃO
1	4 RECIPIENTE(S) P-45 (180 kg), LINHA ÚNICA
2	PIGTAIL (MANGUEIRA DE ALTA PRESSÃO) POR RECIPIENTE
3	COLETOR — TUBULAÇÃO APARENTE NA COR AMARELA (FASE VAPOR)
4	VÁLVULA DE RETENÇÃO NA SAÍDA DO COLETOR
5	TAMPÃO NA EXTREMIDADE DO COLETOR
6	PORTAS INCOMBUSTÍVEIS ABRINDO PARA FORA, COM VENEZIANA EM TODA A EXTENSÃO

DETALHE - REGULADOR DE 1º ESTÁGIO

ESCALA 1:10

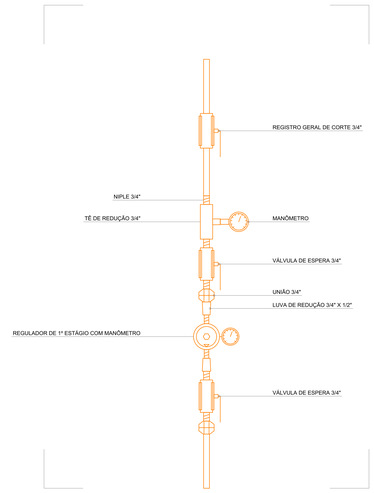

REGULADOR DE 1º ESTÁGIO

NOTAS:


1. REGISTRO GERAL DE CORTE O MAIS PRÓXIMO POSSÍVEL DO LIMITE DA PROPRIEDADE, EM ÁREA COMUM E FORA DA PROJEÇÃO DA EDIFICAÇÃO (NT 3-02, 6.2).
2. REDE DE DISTRIBUIÇÃO INTERNA CONFORME A NBR 15526:2016 (RESIDENCIAL) OU A NBR 15358:2021 (NÃO RESIDENCIAL) (NT 3-02, 6.1).
3. TUBULAÇÃO APARENTE NA COR AMARELA (FASE VAPOR) (NT 3-02, Tabela 1).
4. DIÂMETROS, CLASSE DAS CONEXÕES E PRESSÕES CONFORME O PROJETO DA REDE.

2 DETALHE 5 - REGULADOR DE 1º ESTÁGIO

ESCALA 1:10

DETALHE - REGULADOR DE 2º ESTÁGIO

ESCALA 1:10

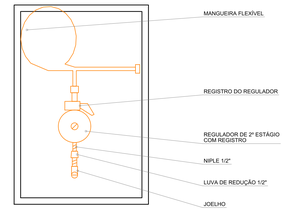

REGULADOR DE 2º ESTÁGIO

INSTALADO NA PAREDE, JUNTO AO PONTO DE CONSUMO

NOTAS:

1. REDE DE DISTRIBUIÇÃO INTERNA CONFORME A NBR 15526:2016 (RESIDENCIAL) OU A NBR 15358:2021 (NÃO RESIDENCIAL) (NT 3-02, 6.1).
2. TUBULAÇÃO APARENTE NA COR AMARELA (FASE VAPOR) (NT 3-02, Tabela 1).
3. REGULADOR, MANGUEIRA E CONEXÕES CONFORME O PROJETO DA REDE E O FABRICANTE.

3 DETALHE 6 - REGULADOR DE 2º ESTÁGIO

ESCALA 1:10

NOTAS

1. Central de 4 x P-45 (premissa do exemplo); diâmetros da rede são premissas (projeto fictício).

PROJETO DE SEGURANÇA CONTRA INCÊNDIO E PÂNICO
RESTAURANTE (F-8) - ATC 400,00 M² - EXEMPLO FICTÍCIO

CONTEÚDO: DETALHES DE GLP

Nº DA PRANCHA: 06 DE 06

PROPRIETÁRIO: PROPRIETÁRIO FICTÍCIO

ENDEREÇO: ENDEREÇO FICTÍCIO

ESCALA:	DATA:	ÁREA:	REVISÃO:
INDICADA	10/11/2026		00

PROPRIETÁRIO
PROPRIETÁRIO FICTÍCIO

O AUTOR DO LEV. ARQUITETÔNICO

O AUTOR DO PROJETO DE SEGURANÇA
PROJETO FICTÍCIO GERADO PELO MOTOR COSCIP

APROVAÇÃO CORPO DE BOMBEIROS:

RASCUNHO GERADO PELO MOTOR COSCIP - SEM VALOR NORMATIVO - SEM RESPONSÁVEL TÉCNICO