
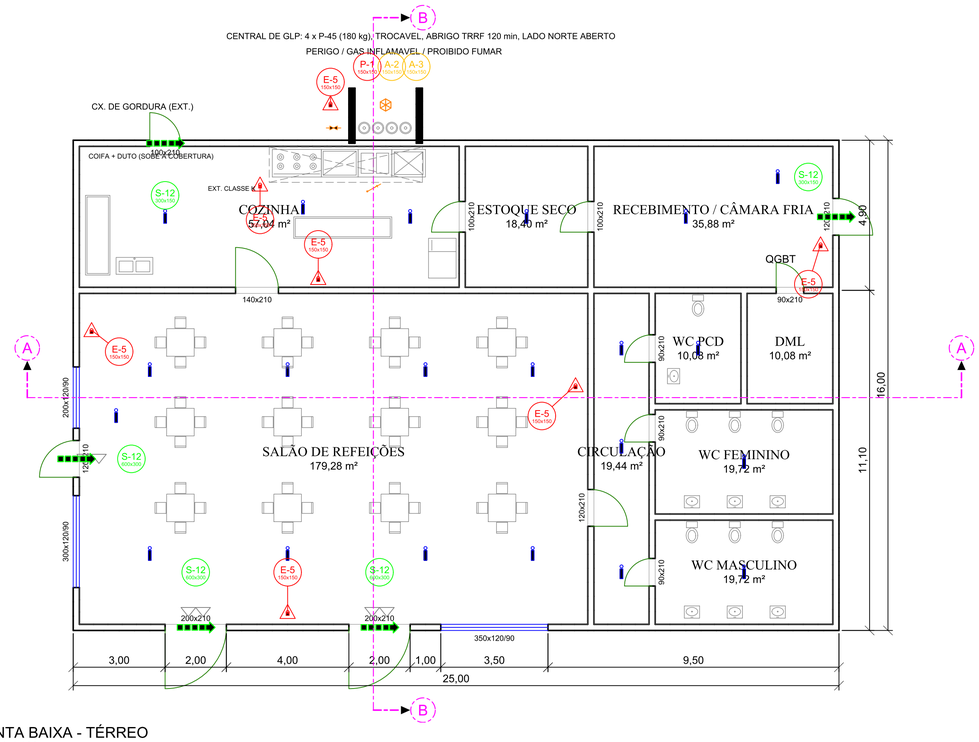


PLANTA BAIXA - TÉRREO
ESCALA 1:100

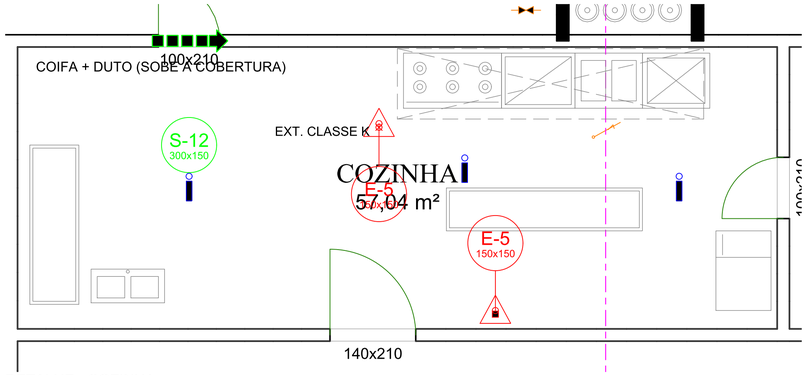

DETALHE - COZINHA
ESCALA 1:50

QUADRO DE ÁREAS


SALÃO DE REFEIÇÕES	179,28 m²
CIRCULAÇÃO	19,44 m²
WC MASCULINO	19,72 m²
WC FEMININO	19,72 m²
WC PCD	10,08 m²
DML	10,08 m²
COZINHA	57,04 m²
ESTOQUE SECO	18,40 m²
RECEBIMENTO / CÂMARA FRIA	35,88 m²
ÁREA ÚTIL TOTAL	369,64 m²
ÁREA CONSTRUÍDA (ATC)	400,00 m²

NOTAS

1. Cotas em metros; etiquetas de porta e janela em centímetros (largura x altura / peitoril).
2. Projeto fictício de exemplo: premissas de ocupação, alturas e tipo de construção não foram confirmadas.
3. Placas de sinalização (NT 2-05): dimensões das chamadas tiradas dos exemplos da Tabela 7; conferir pela distância de visualização.
4. Cozinha: duto de exaustão único e aparente, sem travessia de outros ambientes (NT 3-01, itens 2.1 e 2.2) - a confirmar com o projeto de exaustão.
5. Central de GLP: 4 recipientes P-45 em abrigo com paredes e cobertura TRRF 120 min, lado norte aberto (NT 3-02).

-45 (180 kg), TROCAVEL, ABRIG

IGO / GAS INFLAMAVEL / PROIB

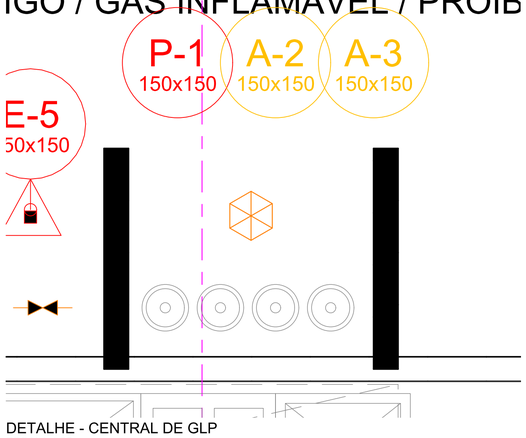

DETALHE - CENTRAL DE GLP
ESCALA 1:25

REV	DATA	DESCRIÇÃO
00	10/11/2026	Emissão inicial (exemplo)

OBRA	PROPRIETÁRIO / REPRESENTANTE LEGAL	AUTOR DO PROJETO E RESPONSÁVEL TÉCNICO	PRANCHA	ESCALA / DATA / REV
RESTAURANTE (F-8) - ATC 400,00 m² - EXEMPLO FICTÍCIO Endereço fictício	Proprietário fictício	Projeto fictício gerado pelo motor COSCIP	PLANTA BAIXA - TÉRREO E DETALHES	ESCALA 1:25 / 1:50 / 1:100 DATA 10/11/2026 REV 00 FOLHA 1/1

RASCUNHO GERADO PELO MOTOR COSCIP - SEM VALOR NORMATIVO - SEM RESPONSÁVEL TÉCNICO