
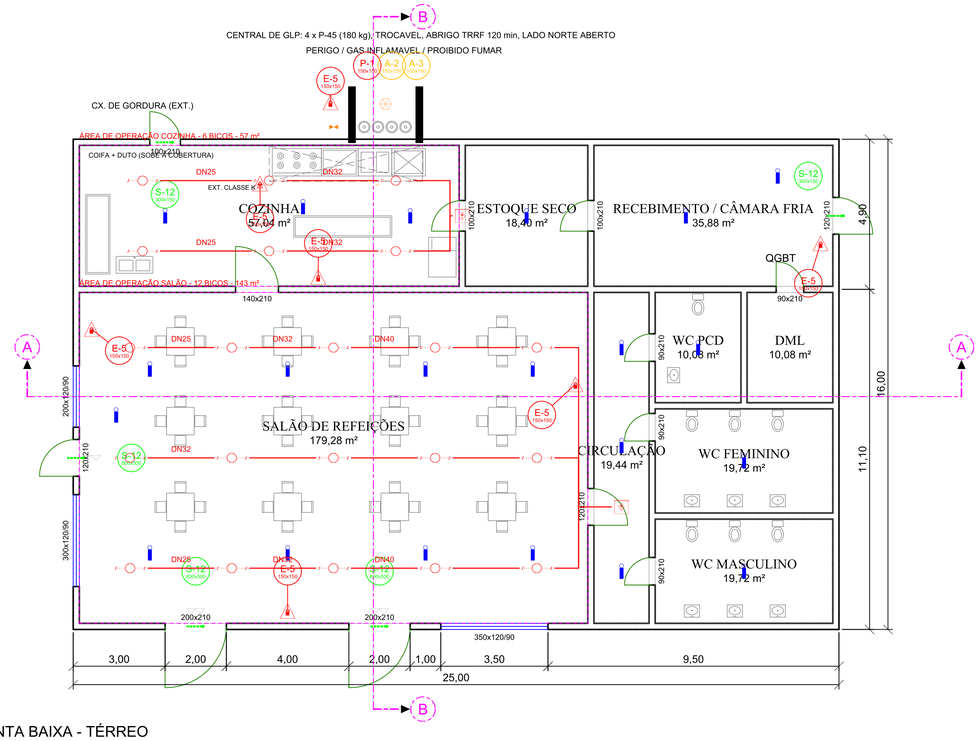



PLANTA BAIXA - TÉRREO
ESCALA 1:100

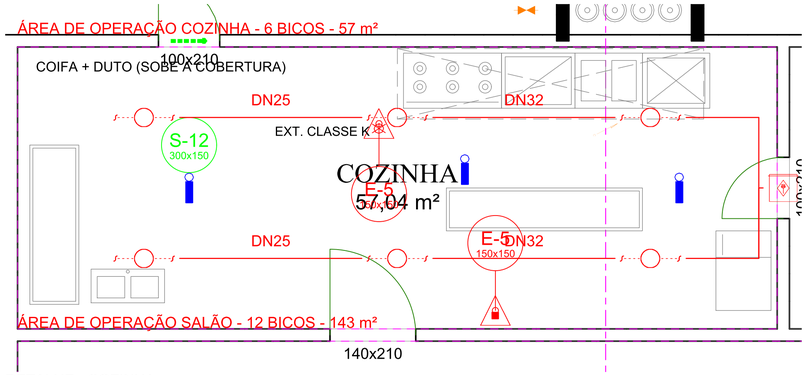

DETALHE - COZINHA
ESCALA 1:50

-45 (180 kg), TROCAVEL, ABRIG

IGO / GAS INFLAMAVEL / PROIB

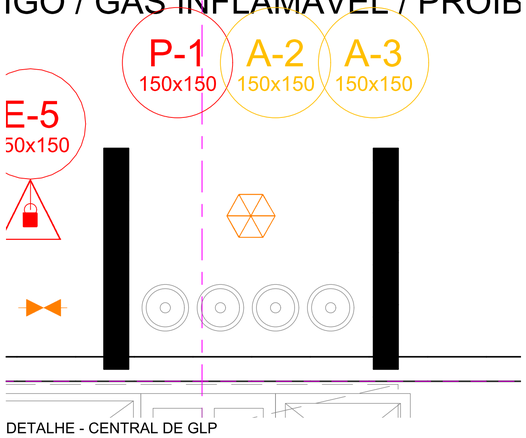

DETALHE - CENTRAL DE GLP
ESCALA 1:25

QUADRO DE ÁREAS

SALÃO DE REFEIÇÕES	179,28 m²
CIRCULAÇÃO	19,44 m²
WC MASCULINO	19,72 m²
WC FEMININO	19,72 m²
WC PCD	10,08 m²
DML	10,08 m²
COZINHA	57,04 m²
ESTOQUE SECO	18,40 m²
RECEBIMENTO / CÂMARA FRIA	35,88 m²
ÁREA ÚTIL TOTAL	369,64 m²
ÁREA CONSTRUÍDA (ATC)	400,00 m²

NOTAS

1. Cotas em metros; etiquetas de porta e janela em centímetros (largura x altura / peitoril).
2. Projeto fictício de exemplo: premissas de ocupação, alturas e tipo de construção não foram confirmadas.
3. Placas de sinalização (NT 2-05): dimensões das chamadas tiradas dos exemplos da Tabela 7; conferir pela distância de visualização.
4. Cozinha: duto de exaustão único e aparente, sem travessia de outros ambientes (NT 3-01, itens 2.1 e 2.2) - a confirmar com o projeto de exaustão.
5. Central de GLP: 4 recipientes P-45 em abrigo com paredes e cobertura TRRF 120 min, lado norte aberto (NT 3-02).

REV	DATA	DESCRIÇÃO
00	10/11/2026	Emissão inicial (exemplo)

OBRA	PROPRIETÁRIO / REPRESENTANTE LEGAL	AUTOR DO PROJETO E RESPONSÁVEL TÉCNICO	PRANCHA	ESCALA / DATA / REV
RESTAURANTE (F-8) - ATC 400,00 m² - EXEMPLO FICTÍCIO Endereço fictício	Proprietário fictício	Projeto fictício gerado pelo motor COSCIP	PLANTA BAIXA - TÉRREO E DETALHES	ESCALA 1:25 / 1:50 / 1:100 DATA 10/11/2026 REV 00 FOLHA 1/4

RASCUNHO GERADO PELO MOTOR COSCIP - SEM VALOR NORMATIVO - SEM RESPONSÁVEL TÉCNICO

QUADRO RESUMO

IDENTIFICAÇÃO DA EDIFICAÇÃO E/OU ÁREA DE RISCO		
Endereço: Endereço fictício		
Proprietário: Proprietário fictício		
Responsável técnico de segurança:		
Conselho técnico:	Nº da matrícula:	
Decreto estadual adotado: Decreto nº 42/2018	Nº de pavimentos: 1	Ocupação do subsolo: Não há
Edificação construída ou licenciada anterior à vigência do Decreto nº 42/2018: SIM ( ) NÃO ( )		Ano de construção:
Lotação prevista: 351 pessoas (NT 2-08, Anexo A)		
Condicionamento de ar:		

CLASSIFICAÇÃO - DECRETO ESTADUAL Nº 42/2018 - ANEXO II			
Grupo	Ocupação	Divisão	Descrição
F	Local de reunião de público	F-8	Local para refeição

CLASSIFICAÇÃO QUANTO À CARGA DE INCÊNDIO - NT 1-04	
Risco: MÉDIO 1 (NT 1-04)	Carga de incêndio (MJ/m²):

ELEMENTOS ESTRUTURAIS - NT 2-19	
Estrutura portante:	
Estrutura de sustentação da cobertura:	
Profundidade do subsolo (m):	TRRF:
Aplicação de revestimento: SIM ( ) NÃO ( )	Material de proteção:

MEDIDAS DE SEGURANÇA CONTRA INCÊNDIO - DECRETO Nº 42/2018
(X) Tabela 2 do Anexo III
(X) Extintores
(X) Saídas de emergência
(X) Iluminação de emergência
(X) Sinalização de segurança
(X) Controle de materiais de acabamento

RISCOS ESPECIAIS - DECRETO Nº 42/2018
(X) Gás liquefeito de petróleo (central externa, NT 3-02)
(X) Cozinha profissional (NT 3-01), a confirmar

GÁS GLP/GN - NT 3-02 (recipientes desenhados)			
Recipiente	Capacidade individual	Nº	Capacidade total
Recipiente P-45	45 kg	4	180 kg
Total		4	180 kg

QUADRO DE ÁREAS (m²)		
Descrição	Térreo	Total
ATC	400,00	400,00
Área útil dos ambientes (do desenho)	369,64	369,64

SISTEMA DE PROTEÇÃO POR EXTINTORES - NT 2-01 (contados no desenho)		
Tipo e capacidade	Térreo	Total
PQS ABC (capacidade não informada)	6	6
Água pressurizada (AP) (capacidade não informada)	1	1
TOTAL	7	7

SISTEMA DE SINALIZAÇÃO DE EMERGÊNCIA - NT 2-05 (contada no desenho)			
Placa	Dimensões (mm)	Térreo	Total
A-2 - Cuidado, risco de incêndio	150x150	1	1
A-3 - Cuidado, risco de explosão	150x150	1	1
E-5 - Extintor de incêndio	150x150	7	7
P-1 - Proibido fumar	150x150	1	1
S-12 - Saída de emergência	300x150	2	2
S-12 - Saída de emergência	600x300	3	3

SISTEMA DE ILUMINAÇÃO DE EMERGÊNCIA - NT 2-06 (contados no desenho)		
Tipo	Térreo	Total
Ponto de iluminação de emergência	21	21

CONTROLE DE MATERIAIS DE ACABAMENTO E REVESTIMENTO - NT 2-20					
Elemento	Acabamento	Classe	Revestimento	Classe	Retardante de chamas
(materiais não informados)					

SAÍDAS DE EMERGÊNCIA - NT 2-08	
Lotação: 351	Tipo de edificação:
Grupo e divisão: F-8	Pavimento: Térreo
Saída única ( ) Mais de uma saída (X)	Tipo de escada: Sem escada
Capacidade da unidade de passagem: 100	Unidades de passagem projetadas: 8 (portas do salão: 3 + 3 + 2)
Saídas desenhadas: 5	Placas de saída desenhadas: 5

Rascunho gerado pelo motor COSCIP: dados informados pelo usuário e contagens do desenho; sem valor normativo.

QUADRO RESUMO
ESCALA 1:100

NOTAS

1. Dados de identificação, classificação, medidas e saídas informados no projeto de exemplo; quantidades de extintores, placas, iluminação, GLP e áreas contadas do desenho.
2. A conferência entre o desenho e os valores declarados está no retorno do motor (quadro_resumo.conferencia).

OBRA
RESTAURANTE (F-8) - ATC 400,00 m² - EXEMPLO FICTÍCIO
Endereço fictício

PROPRIETÁRIO / REPRESENTANTE LEGAL
Proprietário fictício

AUTOR DO PROJETO E RESPONSÁVEL TÉCNICO
Projeto fictício gerado pelo motor COSCIP


PRANCHA
QUADRO RESUMO

ESCALA / DATA / REV
ESCALA 1:100
DATA 10/11/2026
REV 00
FOLHA 2/4

RASCUNHO GERADO PELO MOTOR COSCIP - SEM VALOR NORMATIVO - SEM RESPONSÁVEL TÉCNICO


FACHADA NORTE

ESCALA 1:100

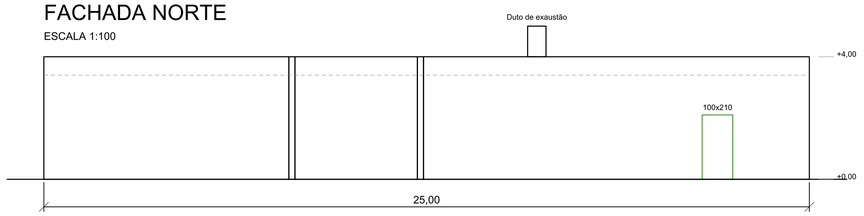


FACHADA SUL

ESCALA 1:100

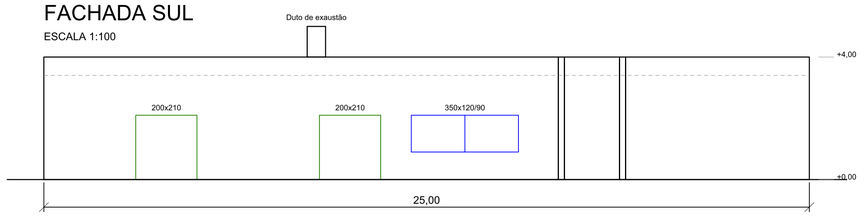


CORTE B-B

ESCALA 1:100

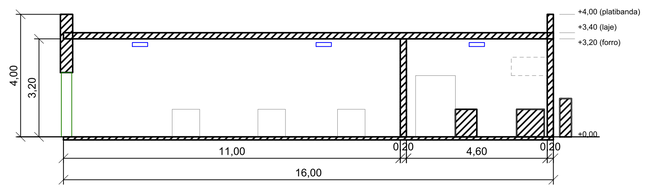

CORTE A-A

ESCALA 1:100

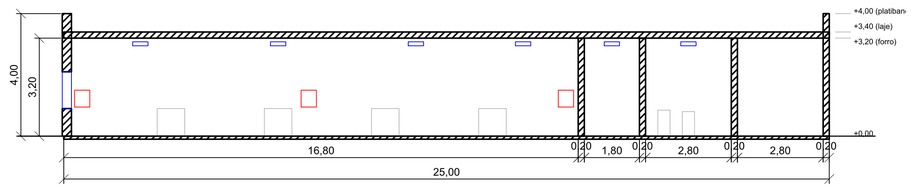

CORTES E FACHADAS

ESCALA 1:100

NOTAS


1. Cortes e fachadas gerados da mesma geometria da planta; alturas e peitoris são premissas do exemplo (projeto fictício).
2. Sem remoção de linhas ocultas.

OBRA	PROPRIETÁRIO / REPRESENTANTE LEGAL	AUTOR DO PROJETO E RESPONSÁVEL TÉCNICO	PRANCHA	ESCALA / DATA / REV
RESTAURANTE (F-8) - ATC 400,00 m² - EXEMPLO FICTÍCIO Endereço fictício	Proprietário fictício	Projeto fictício gerado pelo motor COSCIP	CORTES E FACHADAS	ESCALA 1:100 DATA 10/11/2026 REV 00 FOLHA 3/4

RASCUNHO GERADO PELO MOTOR COSCIP - SEM VALOR NORMATIVO - SEM RESPONSÁVEL TÉCNICO

ISOMÉTRICO DA REDE DE SPRINKLERS - COZINHA

Cozinha - ESCALA 1:100

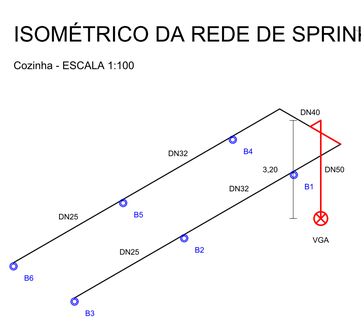

Bico em operação: círculo duplo


QUADRO DE CÁLCULO HIDRÁULICO

TRECHO	DE	PARA	TIPO	DN	L (m)	Q (L/min)	v (m/s)	perda (bar)
T1	J1	B1	ramal	40	1,77	195,1	2,47	0,045
T2	B1	B2	ramal	32	4,13	125,3	2,16	0,099
T3	B2	B3	ramal	25	4,13	60,1	1,80	0,098
T4	J2	B4	ramal	40	1,77	188,2	2,39	0,042
T5	B4	B5	ramal	32	4,13	120,8	2,08	0,092
T6	B5	B6	ramal	25	4,13	58,0	1,74	0,091
T7	J1	J2	subgeral	40	2,30	188,2	2,39	0,055
T8	PR	G1	geral	50	0,40	383,3	2,95	0,011
T9	G1	J1	geral	50	1,15	383,3	2,95	0,031
T10	VGA	PR	prumada	50	3,20	383,3	2,95	0,085

Bicos: 6 em 2 ramais; em operação: 6 (57,04 m²)
Vazão do bico remoto: 57,99 L/min a 0,525 bar
Vazão total: 383,3 L/min
Pressão na base da prumada: 1,547 bar (15,77 mca)
Hazen-Williams, conexões e VGA por premissa (ver memorial)

ISOMÉTRICO DA REDE DE SPRINKLERS - SALÃO

Salão - ESCALA 1:100

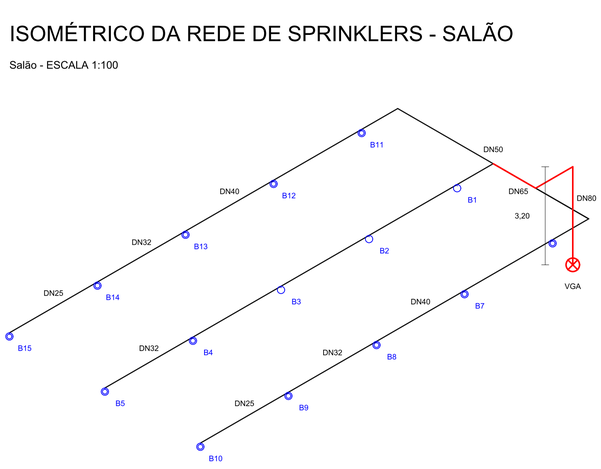

Bico em operação: círculo duplo

QUADRO DE CÁLCULO HIDRÁULICO

TRECHO	DE	PARA	TIPO	DN	L (m)	Q (L/min)	v (m/s)	perda (bar)
T1	J2	B1	ramal	40	1,36	187,5	2,38	0,032
T2	B1	B2	ramal	40	3,32	187,5	2,38	0,079
T3	B2	B3	ramal	40	3,32	187,5	2,38	0,079
T4	B3	B4	ramal	40	3,32	187,5	2,38	0,079
T5	B4	B5	ramal	32	3,32	93,0	1,60	0,046
T6	J1	B6	ramal	50	1,36	441,7	3,40	0,047
T7	B6	B7	ramal	50	3,32	345,6	2,66	0,073
T8	B7	B8	ramal	40	3,32	252,0	3,20	0,137
T9	B8	B9	ramal	32	3,32	163,1	2,81	0,129
T10	B9	B10	ramal	25	3,32	79,0	2,37	0,130
T11	J3	B11	ramal	50	1,36	408,2	3,14	0,041
T12	B11	B12	ramal	50	3,32	319,3	2,46	0,063
T13	B12	B13	ramal	40	3,32	232,7	2,95	0,118
T14	B13	B14	ramal	32	3,32	150,6	2,59	0,111
T15	B14	B15	ramal	25	3,32	72,9	2,19	0,112
T16	J2	J1	subgeral	65	3,60	850,0	4,59	0,176
T17	J1	J3	subgeral	50	7,20	408,2	3,14	0,215
T18	PR	G1	geral	80	1,40	1037,5	3,63	0,034
T19	G1	J2	geral	80	1,60	1037,5	3,63	0,039
T20	VGA	PR	prumada	80	3,20	1037,5	3,63	0,079

Bicos: 15 em 3 ramais; em operação: 12 (143,42 m²)
Vazão do bico remoto: 72,91 L/min a 0,831 bar
Vazão total: 1037,5 L/min
Pressão na base da prumada: 2,432 bar (24,80 mca)
Hazen-Williams, conexões e VGA por premissa (ver memorial)

NOTAS

1. Rede calculada pelo motor: bicos em cascata (K·√P) e Hazen-Williams, tubo de aço classe 40; critérios da classe Ordinário 1 por premissa (NFPA 13), a conferir na norma adotada.
2. Uma prumada por zona neste exemplo; o projeto executivo usa o programa de cálculo do projetista (obstruções, vigas, laços).

ISOMÉTRICOS

ESCALA 1:100

OBRA
RESTAURANTE (F-8) - ATC 400,00 m² - EXEMPLO FICTÍCIO
Endereço fictício

PROPRIETÁRIO / REPRESENTANTE LEGAL
Proprietário fictício

AUTOR DO PROJETO E RESPONSÁVEL TÉCNICO
Projeto fictício gerado pelo motor COSCIP

PRANCHA
SPRINKLERS - ISOMÉTRICOS E CÁLCULO

ESCALA / DATA / REV
ESCALA 1:100
DATA 10/11/2026
REV 00
FOLHA 4/4

RASCUNHO GERADO PELO MOTOR COSCIP - SEM VALOR NORMATIVO - SEM RESPONSÁVEL TÉCNICO