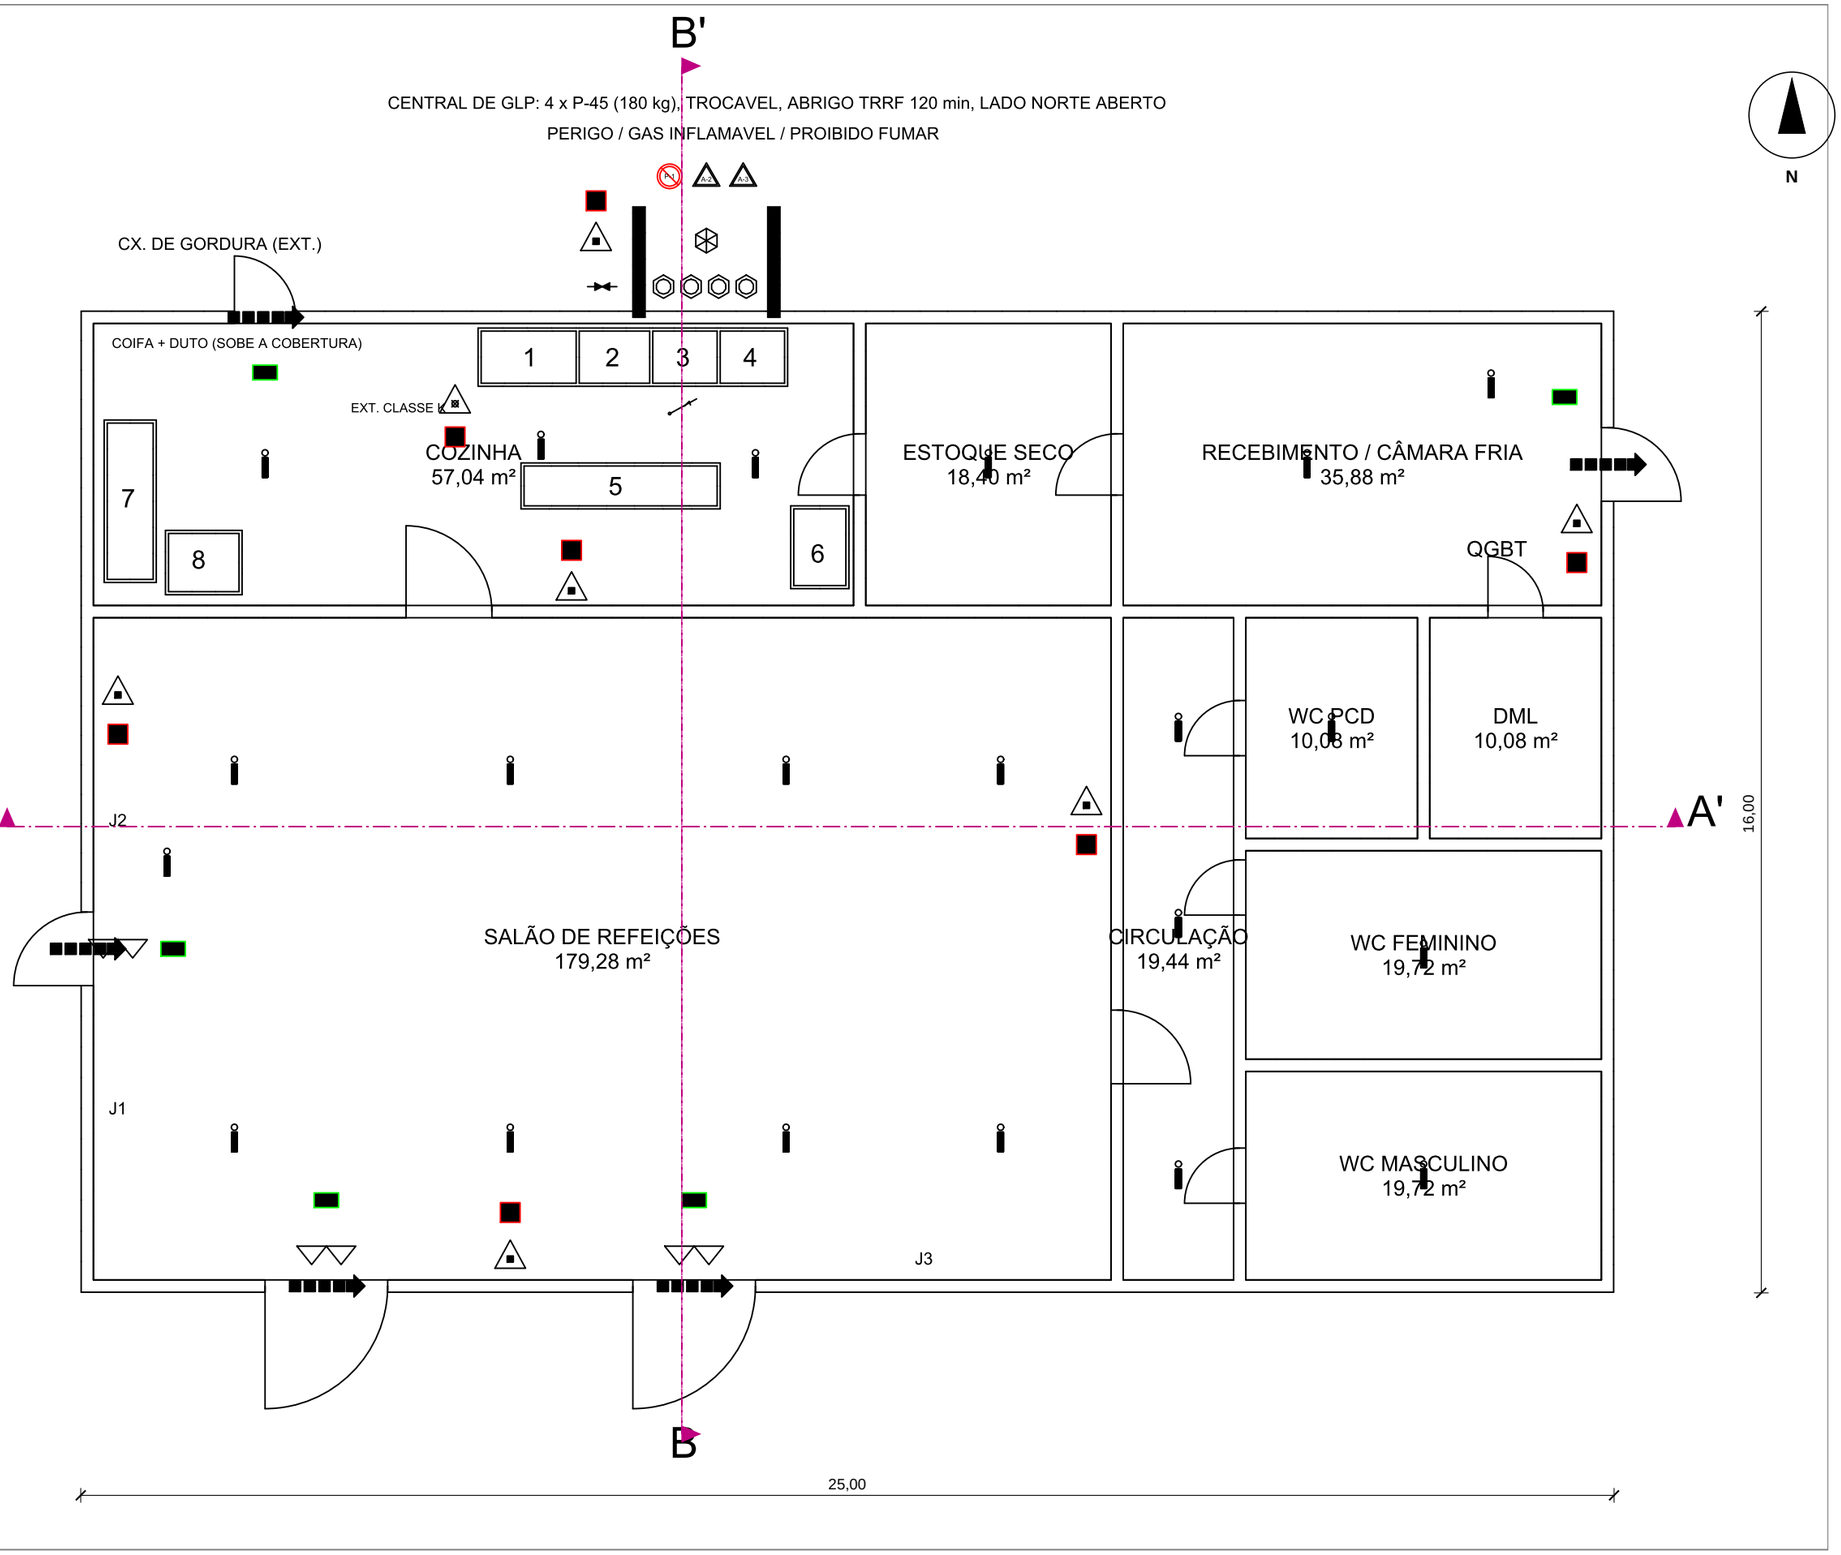


DADOS E RESULTADOS

OCUPACAO: F-8 local para refeicao (premissa: 'restaurante'). Risco MEDIO 1 (NT 1-04).
ATC 400,00 m2; 1 pavimento; altura 4,40 m (premissa); construcao tipo BETA (premissa).

EXIGIDO (Anexo III, Tab. 2): extintores; sinalizacao; iluminacao de emergencia; saidas de emergencia; controle de materiais de acabamento. Hidrante e alarme: nao marcados na tabela.

SAIDAS (NT 2-08): populacao 351 pessoas (350,48 m2 = 400 menos sanitarios, 5.2.4); N = 4 unidades de passagem, largura minima 2,20 m; minimo 2 saidas. Salao: P1 2,00 + P2 2,00 + P3 1,20 = 5,20 m, portas abrindo para fora com barra antipanico (lotacao > 200). Servico: P4 cozinha 1,00 m e P5 recebimento 1,20 m.

EXTINTORES (NT 2-01): 3 pela area (150 m2 por unidade) + 2 instalacoes especiais = 5 calculados; 7 desenhados (E1-E5 PQS ABC, K na cozinha, E6 central de GLP).

ILUMINACAO (NT 2-06): 21 pontos, autonomia 60 min.

MOTOR COSCIP (unidade confirmada por 2 medidas de projeto): maior percurso ate extintor 12,8 m (+/- 0,6) para limite de 15 m; ate a saida 16,5 m (+/- 0,6) para limite de 30 m (Anexo C, BETA, 2 saidas, leiaute definido); distancia direta 13,3 m. Verificacao do percurso ate a saida depende de o usuario confirmar as saidas.

COZINHA E GLP: ver pranchas 02 e 03 e o memorial (NT 3-01 e NT 3-02).

NAO CONSTA DA PLANTA: projeto de exaustao (NBR 14518), espacamento da iluminacao (NBR 10898), implantacao do lote e distancia ao passeio.

RESTAURANTE (F-8) - ATC 400,00 m2 - 1 PAVIMENTO

Projeto de seguranca contra incendio e panico (COSCIP/CBMERJ) - RASCUNHO

PROJETO FICTICIO - sem valor normativo - nao protocolar - sem responsavel tecnico

Dados de ocupacao, alturas e tipo de construcao sao premissas. Gerado em 09/11/2026 pelo motor COSCIP.

PRANCHA

PLANTA BAIXA - TERREO


ESCALA

1:100

FOLHA


01/03

CORTE A-A (olhando para o norte)

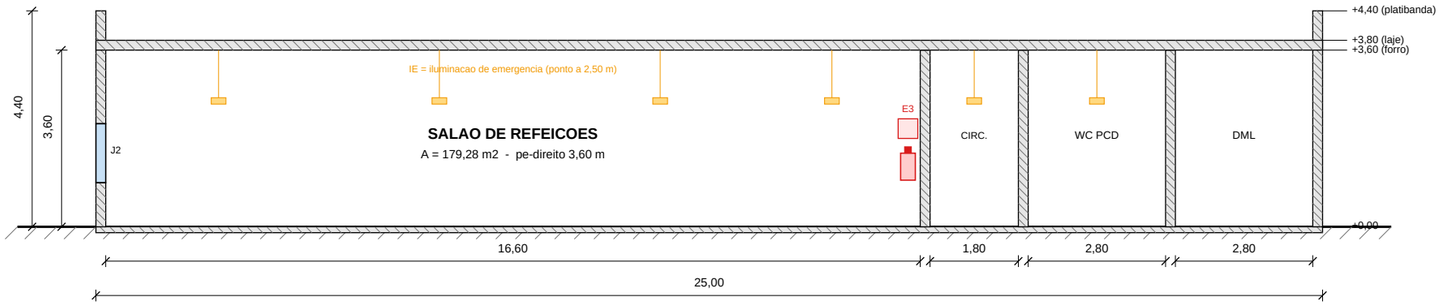

Esc. 1:125 - cota de piso +0,00 - esquematico, sem estrutura


CORTE B-B (olhando para o leste)

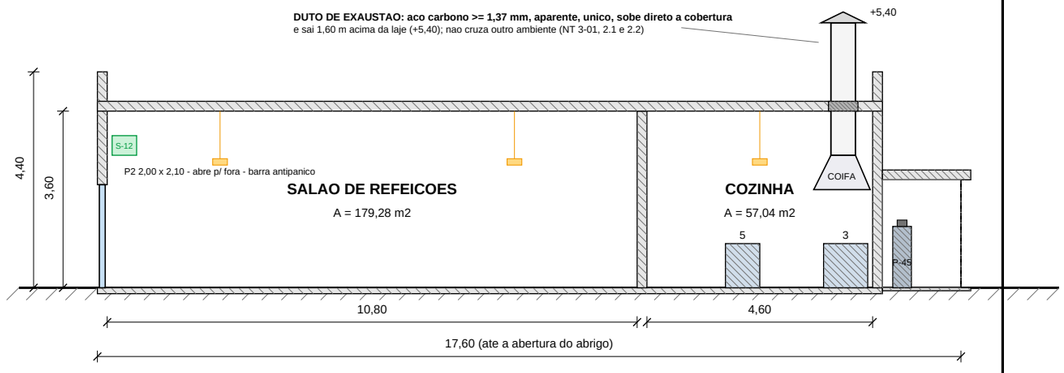


CENTRAL DE GLP (abrigo a direita): 4 x P-45 = 180 kg; abrigo TRRF 120 min (5.3.2 b); altura util 2,20 m;
piso de concreto >= 5 cm; lado norte aberto com portas incombustiveis p/ fora; ventilacao 10% da planta (0,32 m2)

Esc. 1:125 - esquematico; pe-direito 3,60 m; laje 0,20 m


FACHADA SUL (frontal)

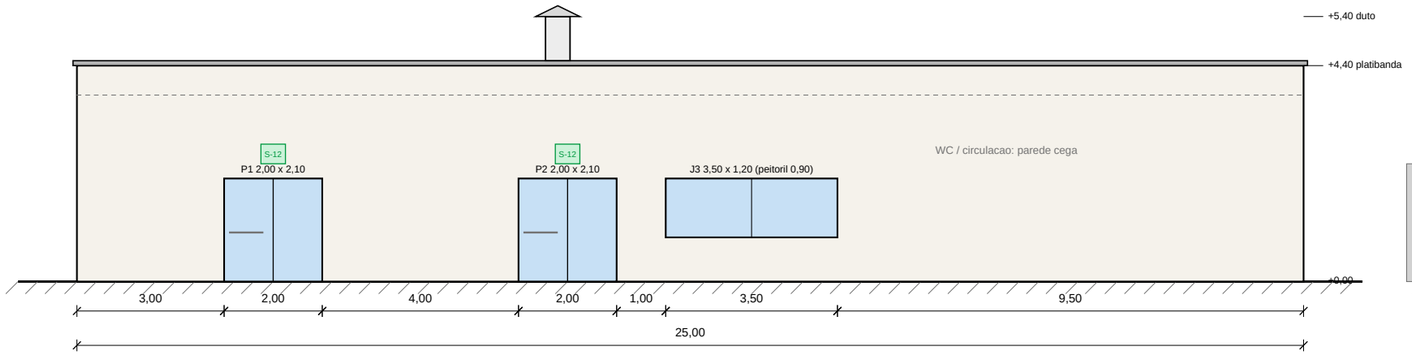


FACHADA OESTE

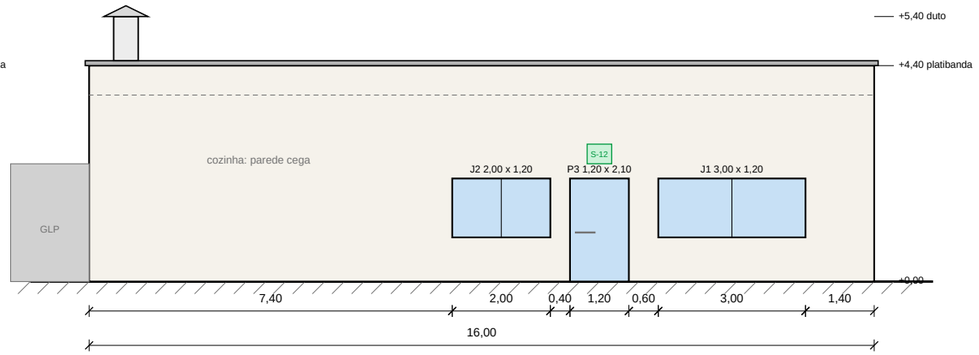

FACHADA NORTE (fundos)

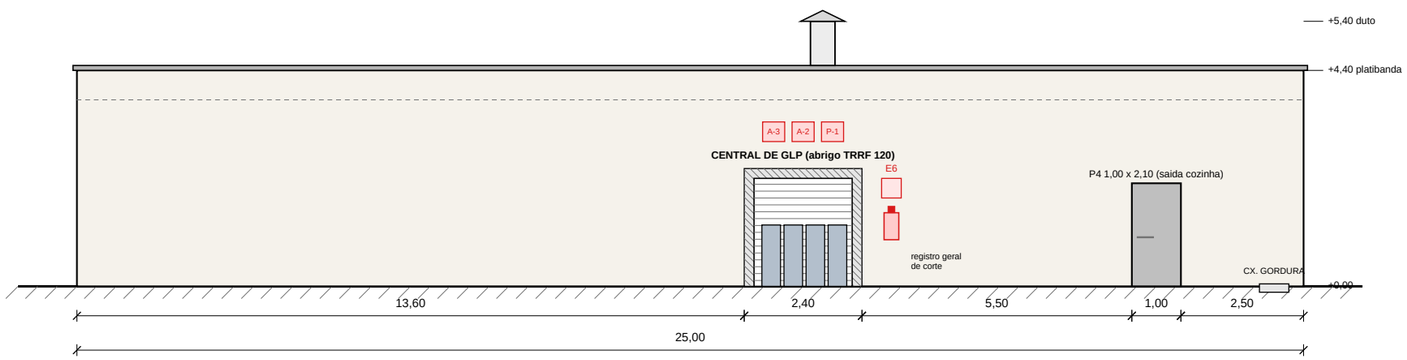

FACHADA LESTE

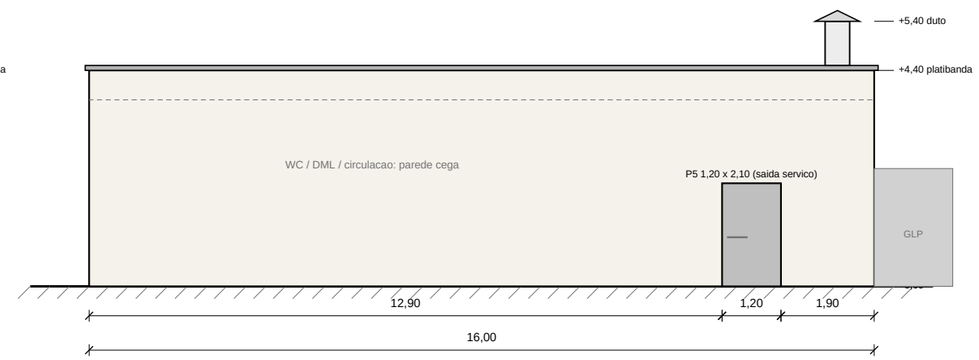

NOTAS: pe-direito 3,60 m; laje de cobertura 0,20 m (+3,80); platibanda +4,40 m. Alturas, esquadrias e dimensoes do abrigo sao premissas do projeto ficticio, desenhadas de forma esquematica a partir da planta baixa (prancha 01). Cortes A-A (y = 7,60) e B-B (x = 9,80) marcados na planta. Duto de exaustao: unico, vertical, sem travessia de outros ambientes (NT 3-01, 2.1 e 2.2); projeto de exaustao pela ABNT NBR 14518 fica a cargo do responsavel tecnico. Portas de saida do salao abrem para fora (NT 2-08, 5.3.4.1).

RESTAURANTE (F-8) - ATC 400,00 m2 - 1 PAVIMENTO

Projeto de seguranca contra incendio e panico (COSCIP/CBMERJ) - RASCUNHO

PROJETO FICTICIO - sem valor normativo - nao protocolar - sem responsavel tecnico

Dados de ocupacao, alturas e tipo de construcao sao premissas. Gerado em 09/11/2026 pelo motor COSCIP.

PRANCHA	ESCALA	FOLHA
CORTES E FACHADAS	**1:125**	**02/03**

LEGENDA DOS SIMBOLOS (NT 1-03 e NT 2-05)

LEGENDA

- EXTINTOR DE PÓ ABC
- E-5 - Extintor de incêndio
- S-12 - Saída de emergência
- BARRA ANTIPÂNICO
- SAÍDA FINAL
- PONTO DE ILUMINAÇÃO DE EMERGÊNCIA
- DIVISÓRIA
- EXTINTOR DE ÁGUA PRESSURIZADA - AP
- PAREDE CORTA-FOGO
- VASO PRESSÃO
- CENTRAL DE GLP
- REGISTRO
- P-1 - Proibido fumar
- A-2 - Cuidado, risco de incêndio
- A-3 - Cuidado, risco de explosão
- TUBO QUE SOBE

EQUIPAMENTOS DA COZINHA

1 Fogao 6 bocas (GLP) - equipamento moderado
2 Chapa de grelhados (GLP) - severo
3 Fritadeira 2 cubas (GLP) - moderado
4 Forno combinado (GLP) - moderado
5 Ilha de preparo
6 Refrigeracao
7 Pia de panelas
8 Lava-loucas

Sob a mesma coifa ha equipamento moderado e severo: exaustao Tipo I (NT 3-01, 5.5.1). Edificacao de economia unica. Coifa + duto unico, aparente, sobe a cobertura. Extintor classe K junto a linha de coccao (distancia maxima 10 m, NT 2-01 Tab. 5); a NT 1-03 nao tem simbolo para classe K: na planta ele usa o simbolo do extintor AP, com a anotacao 'EXT. CLASSE K'.

QUADRO DE EXTINTORES (NT 2-01 e NT 3-02)

ID	TIPO / CAPACIDADE	LOCAL	POSICAO x ; y (m)
E1	PQS ABC 2-A:20-B:C	Salao - parede sul entre as portas	7,00 ; 0,60
E2	PQS ABC 2-A:20-B:C	Salao - parede oeste, lado norte	0,60 ; 9,80
E3	PQS ABC 2-A:20-B:C	Salao - parede leste, junto a circulacao	16,40 ; 8,00
E4	PQS ABC 2-A:20-B:C	Cozinha - junto a porta do salao	8,00 ; 11,50
K	Classe K (a criterio do projetista)	Cozinha - extremo oeste da linha de coccao	6,10 ; 14,55
E5	PQS ABC 2-A:20-B:C	Recebimento - saida de servico e QGBT (<= 5 m)	24,40 ; 12,60
E6	PQS 6 kg (20-B:C)	Central de GLP (<= 10 m, NT 3-02 5.4.2)	8,40 ; 17,20

Calculo (NT 2-01): risco MEDIO; area 400 m2 / 150 m2 por unidade = 3; minimo 2; + 1 por instalacao especial (GLP e quadro eletrico) = 5. Desenhados 7 (E4 e K acrescentados para a cozinha). Altura maxima da alca 1,60 m; distancia maxima a percorrer 15 m (K: 10 m). Cada extintor leva placa E-5 (NT 2-05). Medido pelo motor: maior percurso ate um extintor 12,8 m (+/- 0,6).

SAIDAS, ILUMINACAO E SINALIZACAO

SAIDAS (NT 2-08): populacao 351 pessoas (area 350,48 m2 = 400 menos sanitarios 49,52 m2, 1 pessoa/m2); N = 4 unidades de passagem; largura minima de acessos 2,20 m; minimo 2 saidas (grupo F). Salao: P1 2,00 m, P2 2,00 m e P3 1,20 m = 5,20 m, abrindo para fora, com barra antipanico (lotacao > 200, 5.3.4.9). Servico: P4 (cozinha) 1,00 m e P5 (recebimento) 1,20 m. Limite de percurso 30 m (Anexo C, BETA, 2 saidas, leiaute definido); medido 16,5 m (+/- 0,6).

ILUMINACAO DE EMERGENCIA (NT 2-06): 21 pontos ao longo das rotas, portas de saida, corredor, sanitarios, cozinha e recebimento; autonomia 60 min. Espacamento e iluminamento pela NBR 10898 (fora da base): a definir.

SINALIZACAO (NT 2-05): S-12 sobre as 5 saidas; E-5 em cada extintor; P-1, A-2 e A-3 e a placa PERIGO / GAS INFLAMAVEL / PROIBIDO FUMAR na central de GLP.

CENTRAL DE GLP (NT 3-02)

4 x P-45 trocaveis = 180 kg (0,432 m3), em linha unica, no terreo, fora da projecao da edificacao, junto a fachada norte (5.2.1). Abrigo com paredes e cobertura TRRF >= 120 min (acima de 90 kg, 5.3.2 b), piso de concreto >= 5 cm, altura util 2,20 m (>= 1,80), lado maior aberto com portas incombustiveis para fora e ventilacao >= 0,32 m2 (10% da planta de 3,20 m2). Afastamentos (Anexo A): edificacao 0 m; aberturas e fontes de ignicao 1,5 m (reduzivel a metade com o abrigo); caixa de gordura >= 1,0 m (esta a mais de 8 m); passeio publico 3 m (depende do lote). Extintor 20-B:C ate 10 m (E6 a cerca de 2 m). Registro geral de corte junto a central (6.2). Sem hidrante exigido, resfriamento ou SPDA.

PENDENCIAS E PREMISSAS (revisao do responsavel tecnico)

- Ocupacao F-8, 1 pavimento, 400 m2, altura 4,40 m e construcao tipo BETA sao premissas minhas; as saidas nao foram confirmadas pelo usuario.
- Cozinha: confirmar que o duto nao cruza outro ambiente; se cruzar, aplicar damper corta-fogo, selagem e protecao passiva (Tabela 2 da NT 3-01; sem sistema fixo na economia unica). Dimensionar o extintor classe K.
- GLP: ART da central e do ensaio de estanqueidade (5.3.9, 6.4), nota no Quadro Resumo (8.2), representacao em corte e planta de situacao, distancia ao lote.
- Esquadrias J1 a J3 so existem como texto na planta (o motor nao desenha janelas); conferir a observacao 4 da Tabela 2 (edificacoes sem janelas).
- Fora da base do motor: NBR 14518 (exaustao), NBR 10898 (iluminacao), NBR 13523 e NBR 15358 (GLP). Controle de materiais de acabamento (NT 2-20) e plano de emergencia nao detalhados.
- Barras antipanico aparecem desenhadas mas o motor nao as conta como equipamento.

RESTAURANTE (F-8) - ATC 400,00 m2 - 1 PAVIMENTO

Projeto de seguranca contra incendio e panico (COSCIP/CBMERJ) - RASCUNHO

PROJETO FICTICIO - sem valor normativo - nao protocolar - sem responsavel tecnico

Dados de ocupacao, alturas e tipo de construcao sao premissas. Gerado em 09/11/2026 pelo motor COSCIP.

PRANCHA: **LEGENDA, QUADROS E NOTAS**

ESCALA: **S/ ESC.**

FOLHA: **03/03**